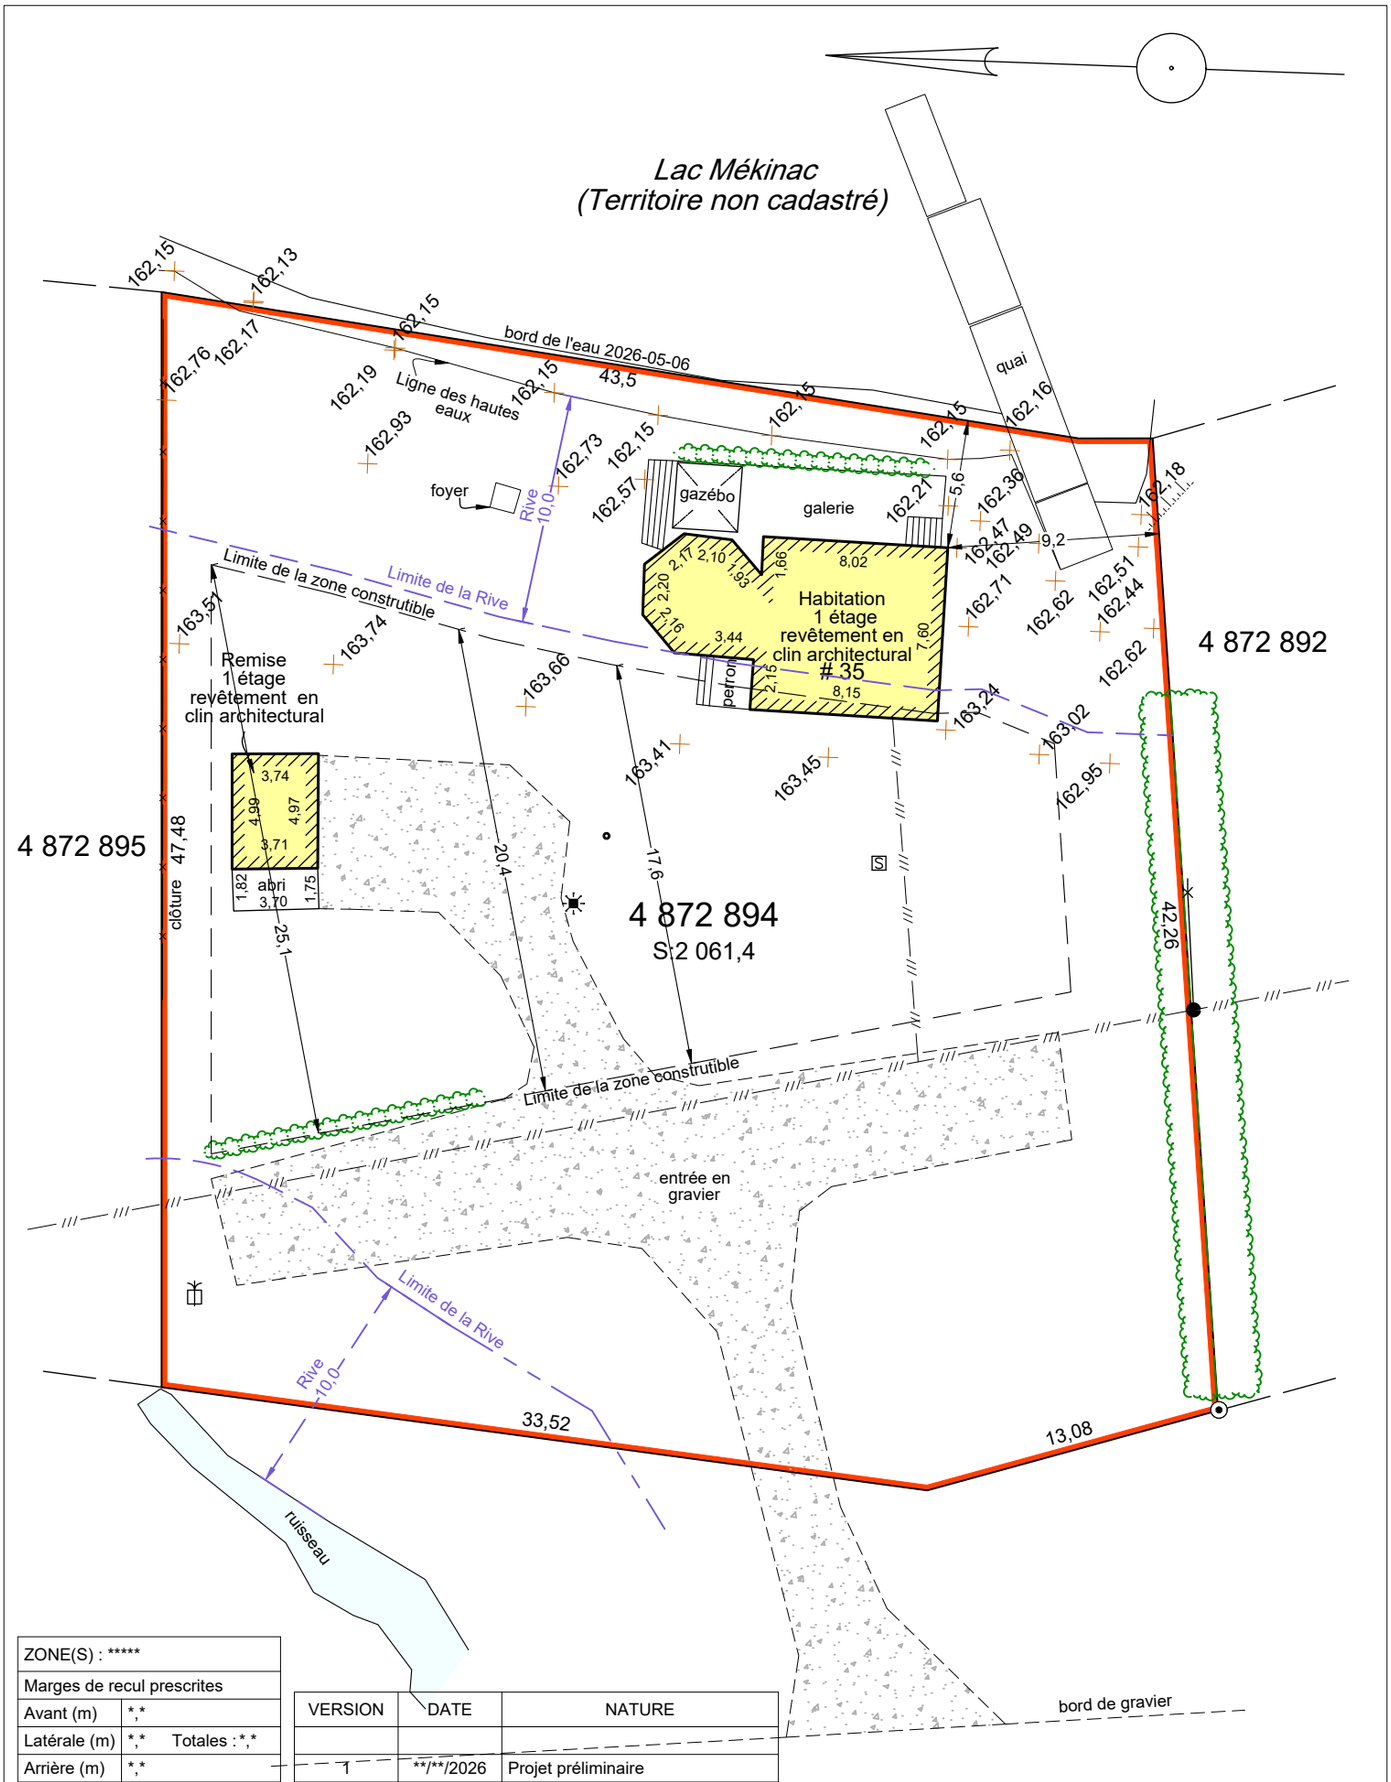

ZONE(S) : *****		
Marges de recul prescrites		
Avant (m)	*,*	
Latérale (m)	*,*	Totales : *,*
Arrière (m)	*,*	

VERSION	DATE	NATURE
1	**/**/2026	Projet préliminaire

PROJET D'IMPLANTATION

Ce plan a été effectué dans le but de positionner la/les future(s) structure(s) sur la propriété pour le seul bénéfice du client ou de son mandant. Ce plan ne peut être utilisé pour une autre fin que celle à laquelle il est destiné.

Date de levé des lieux : 6 mai 2026
N.B. Sujet à l'approbation municipale
N.B. Les mesures indiquées sur ce document sont en mètres (S.I.)

GÉOMATIQUE BLP
ARPENTEURS-GÉOMÈTRES INC.
Trois-Rivières : (819) 374-2431
(Secteur Cap) : (819) 373-0313
Shawinigan : (819) 536-0833
Bécancour : (819) 294-1248
info@blpag.com

Lot(s) : 4 872 894

Cadastre : du Québec

Municipalité : Trois-Rives

Circonscription foncière : Shawinigan

Zonage municipal : 71-Va

Client : Martin Avoine

Trois-Rivières, le DATE_MINUTE

FRANÇOIS HARVEY
ARPENTEUR-GÉOMÈTRE

Échelle: 1 : 300	Dossier : 26-0687	Minute : MINUTE

CD